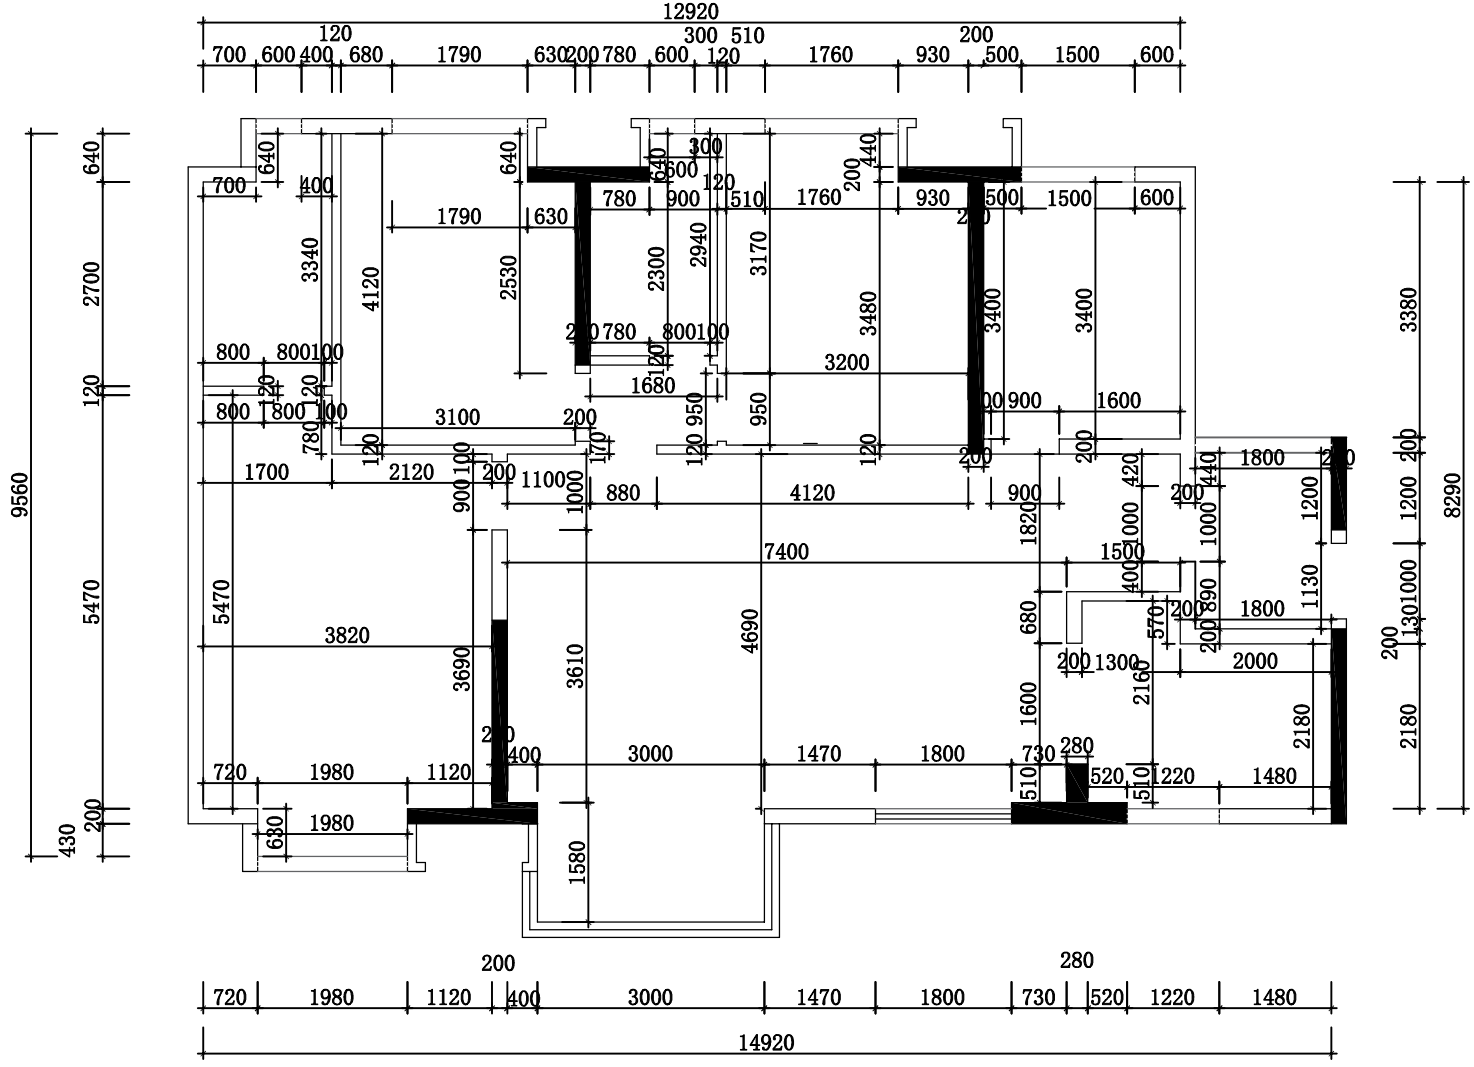


PL-1F-02 1F墙体定位尺寸图

SCALE 1:100

INTERIOR DESIGN

PROJECT NAME

空间设计

PROJECT
项目名称:

EXPLAIN

此图仅供施工单位作总体内部布置使用有责任现场核实所有尺寸，此图根据有效的信息制成，但在具体工程应用时应核实。在确定最终细部和装配前应对此图进行审核。此图所有权属本公司所有，严禁复制拷贝。

此图仅用于此特定的工程，不适用于其他工程。如若要求归还此图，请予以归还。

设 计:
制 图:
校 对:
审 核:
日 期:
比 例:

DRAWING NO.
图纸名称:
墙体定位尺寸图

图纸编号:
PL-1F-02